



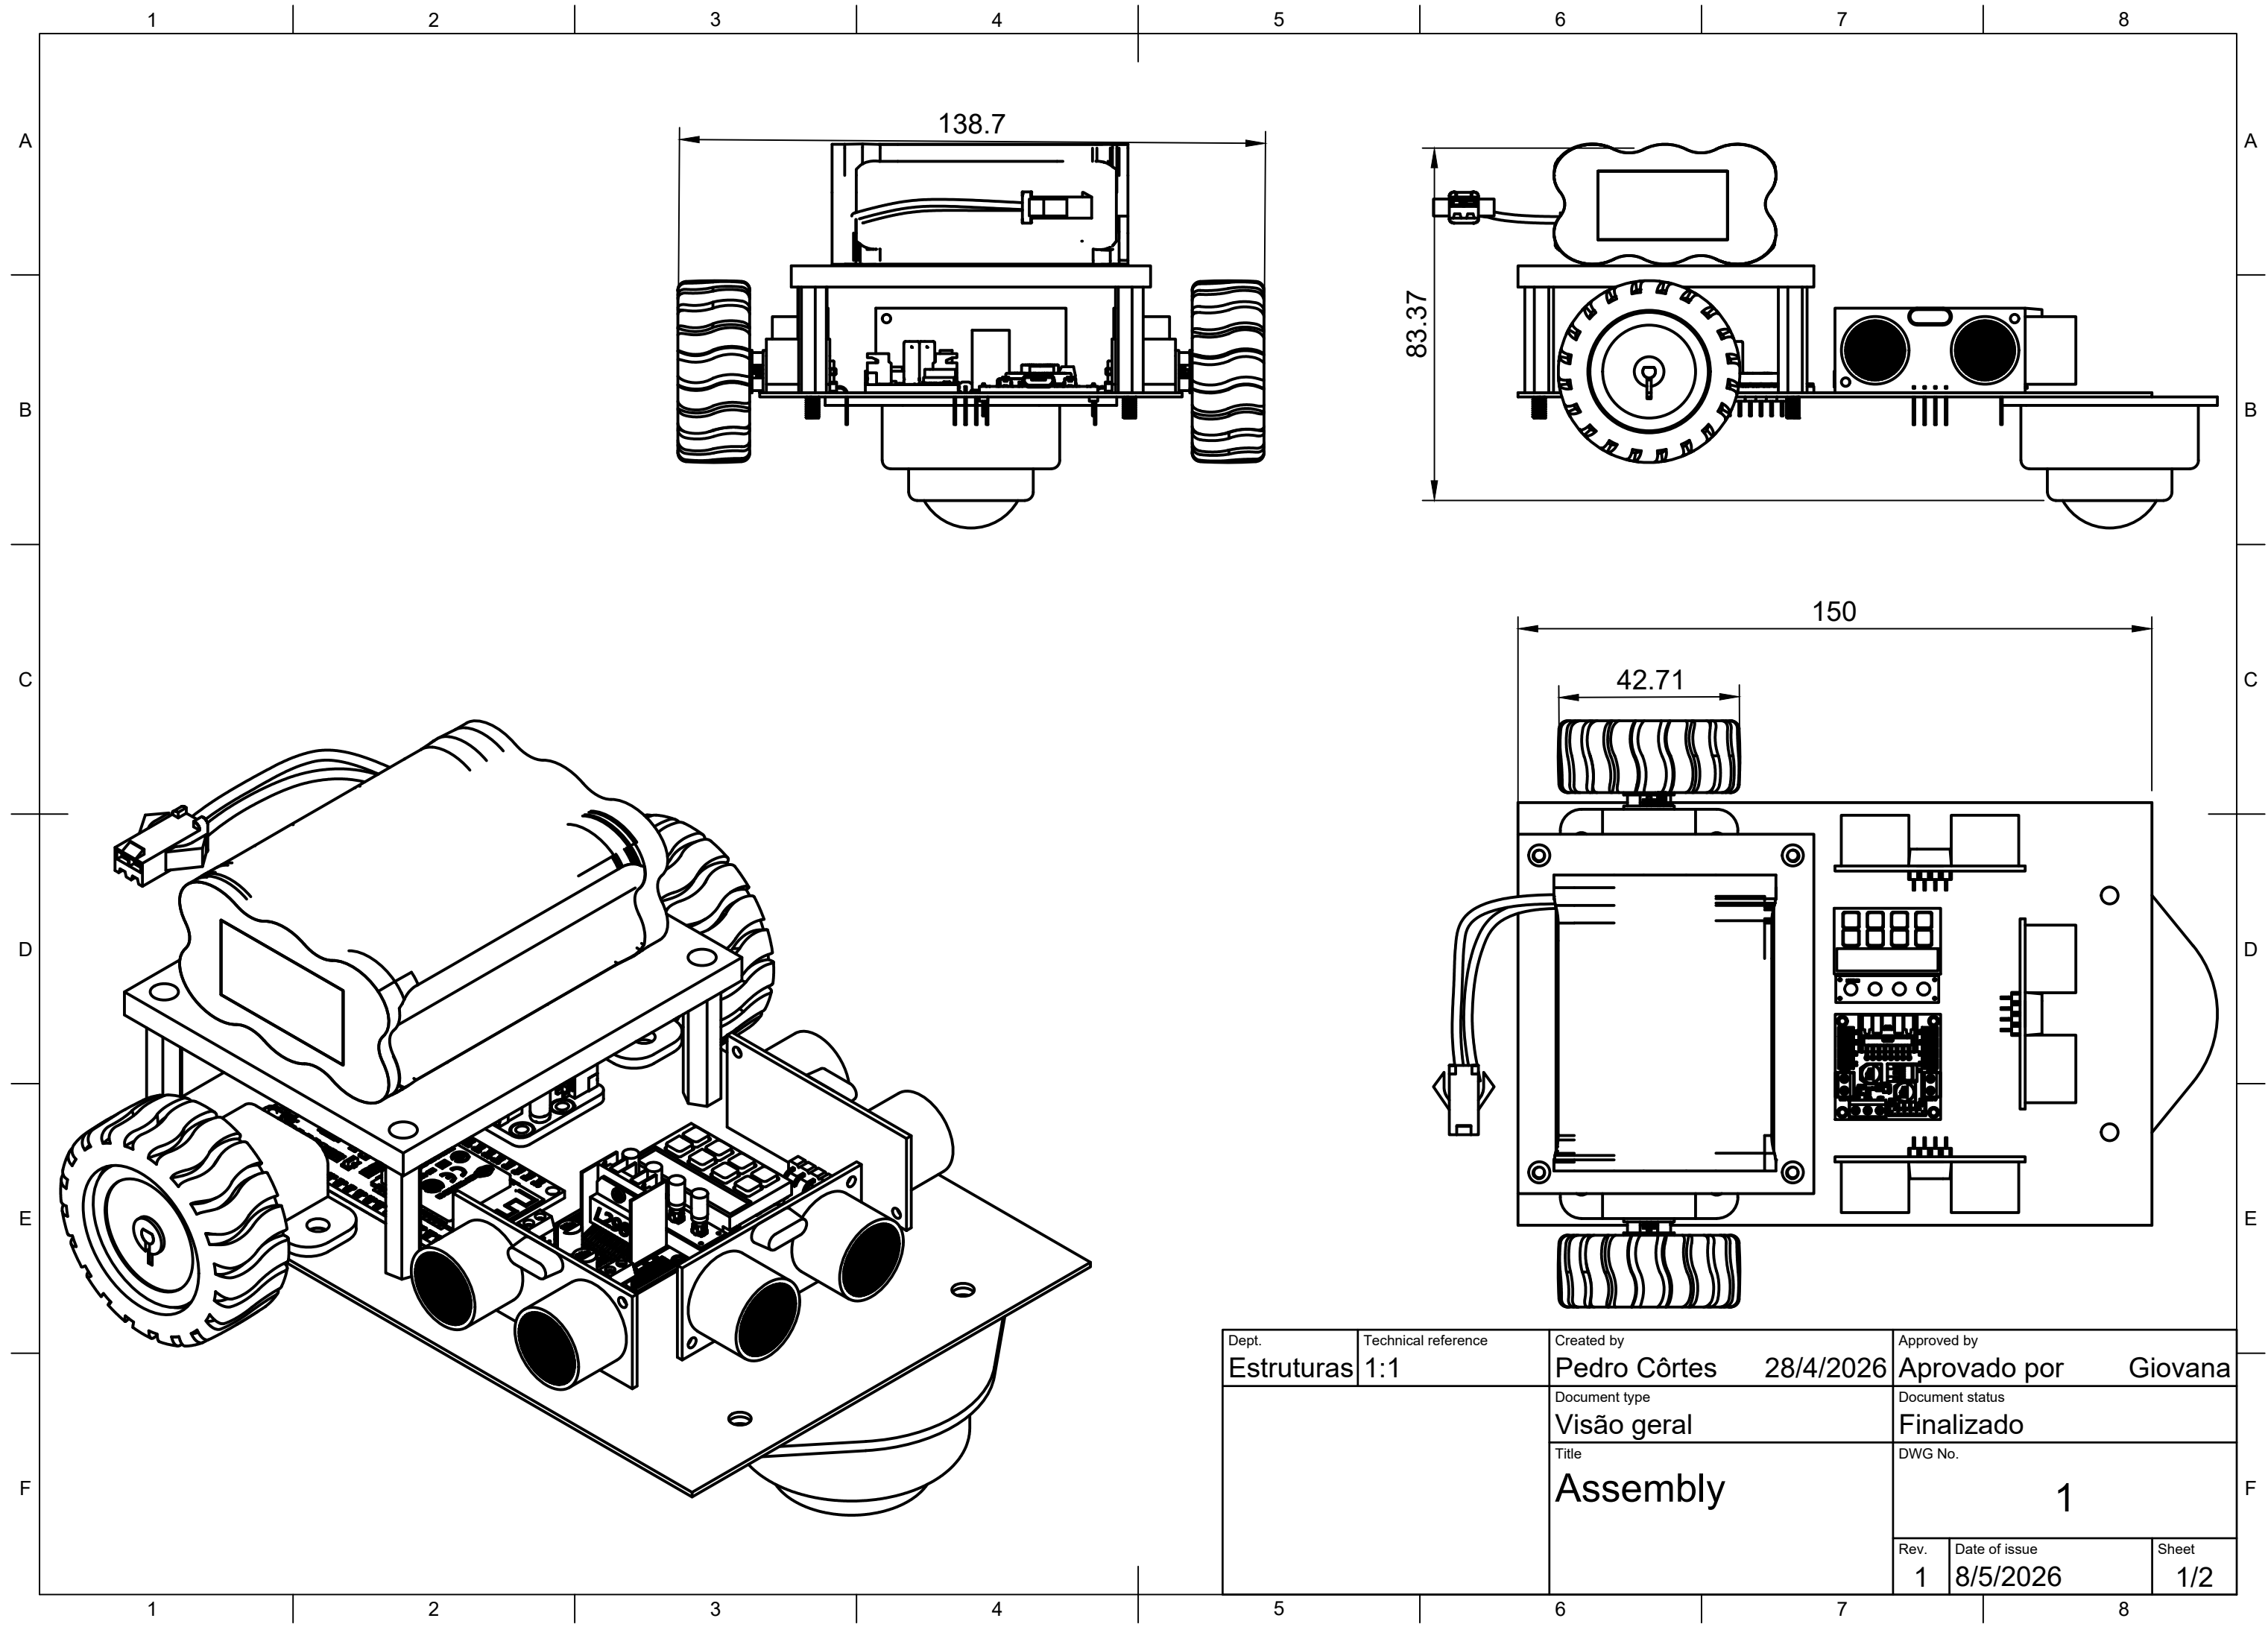

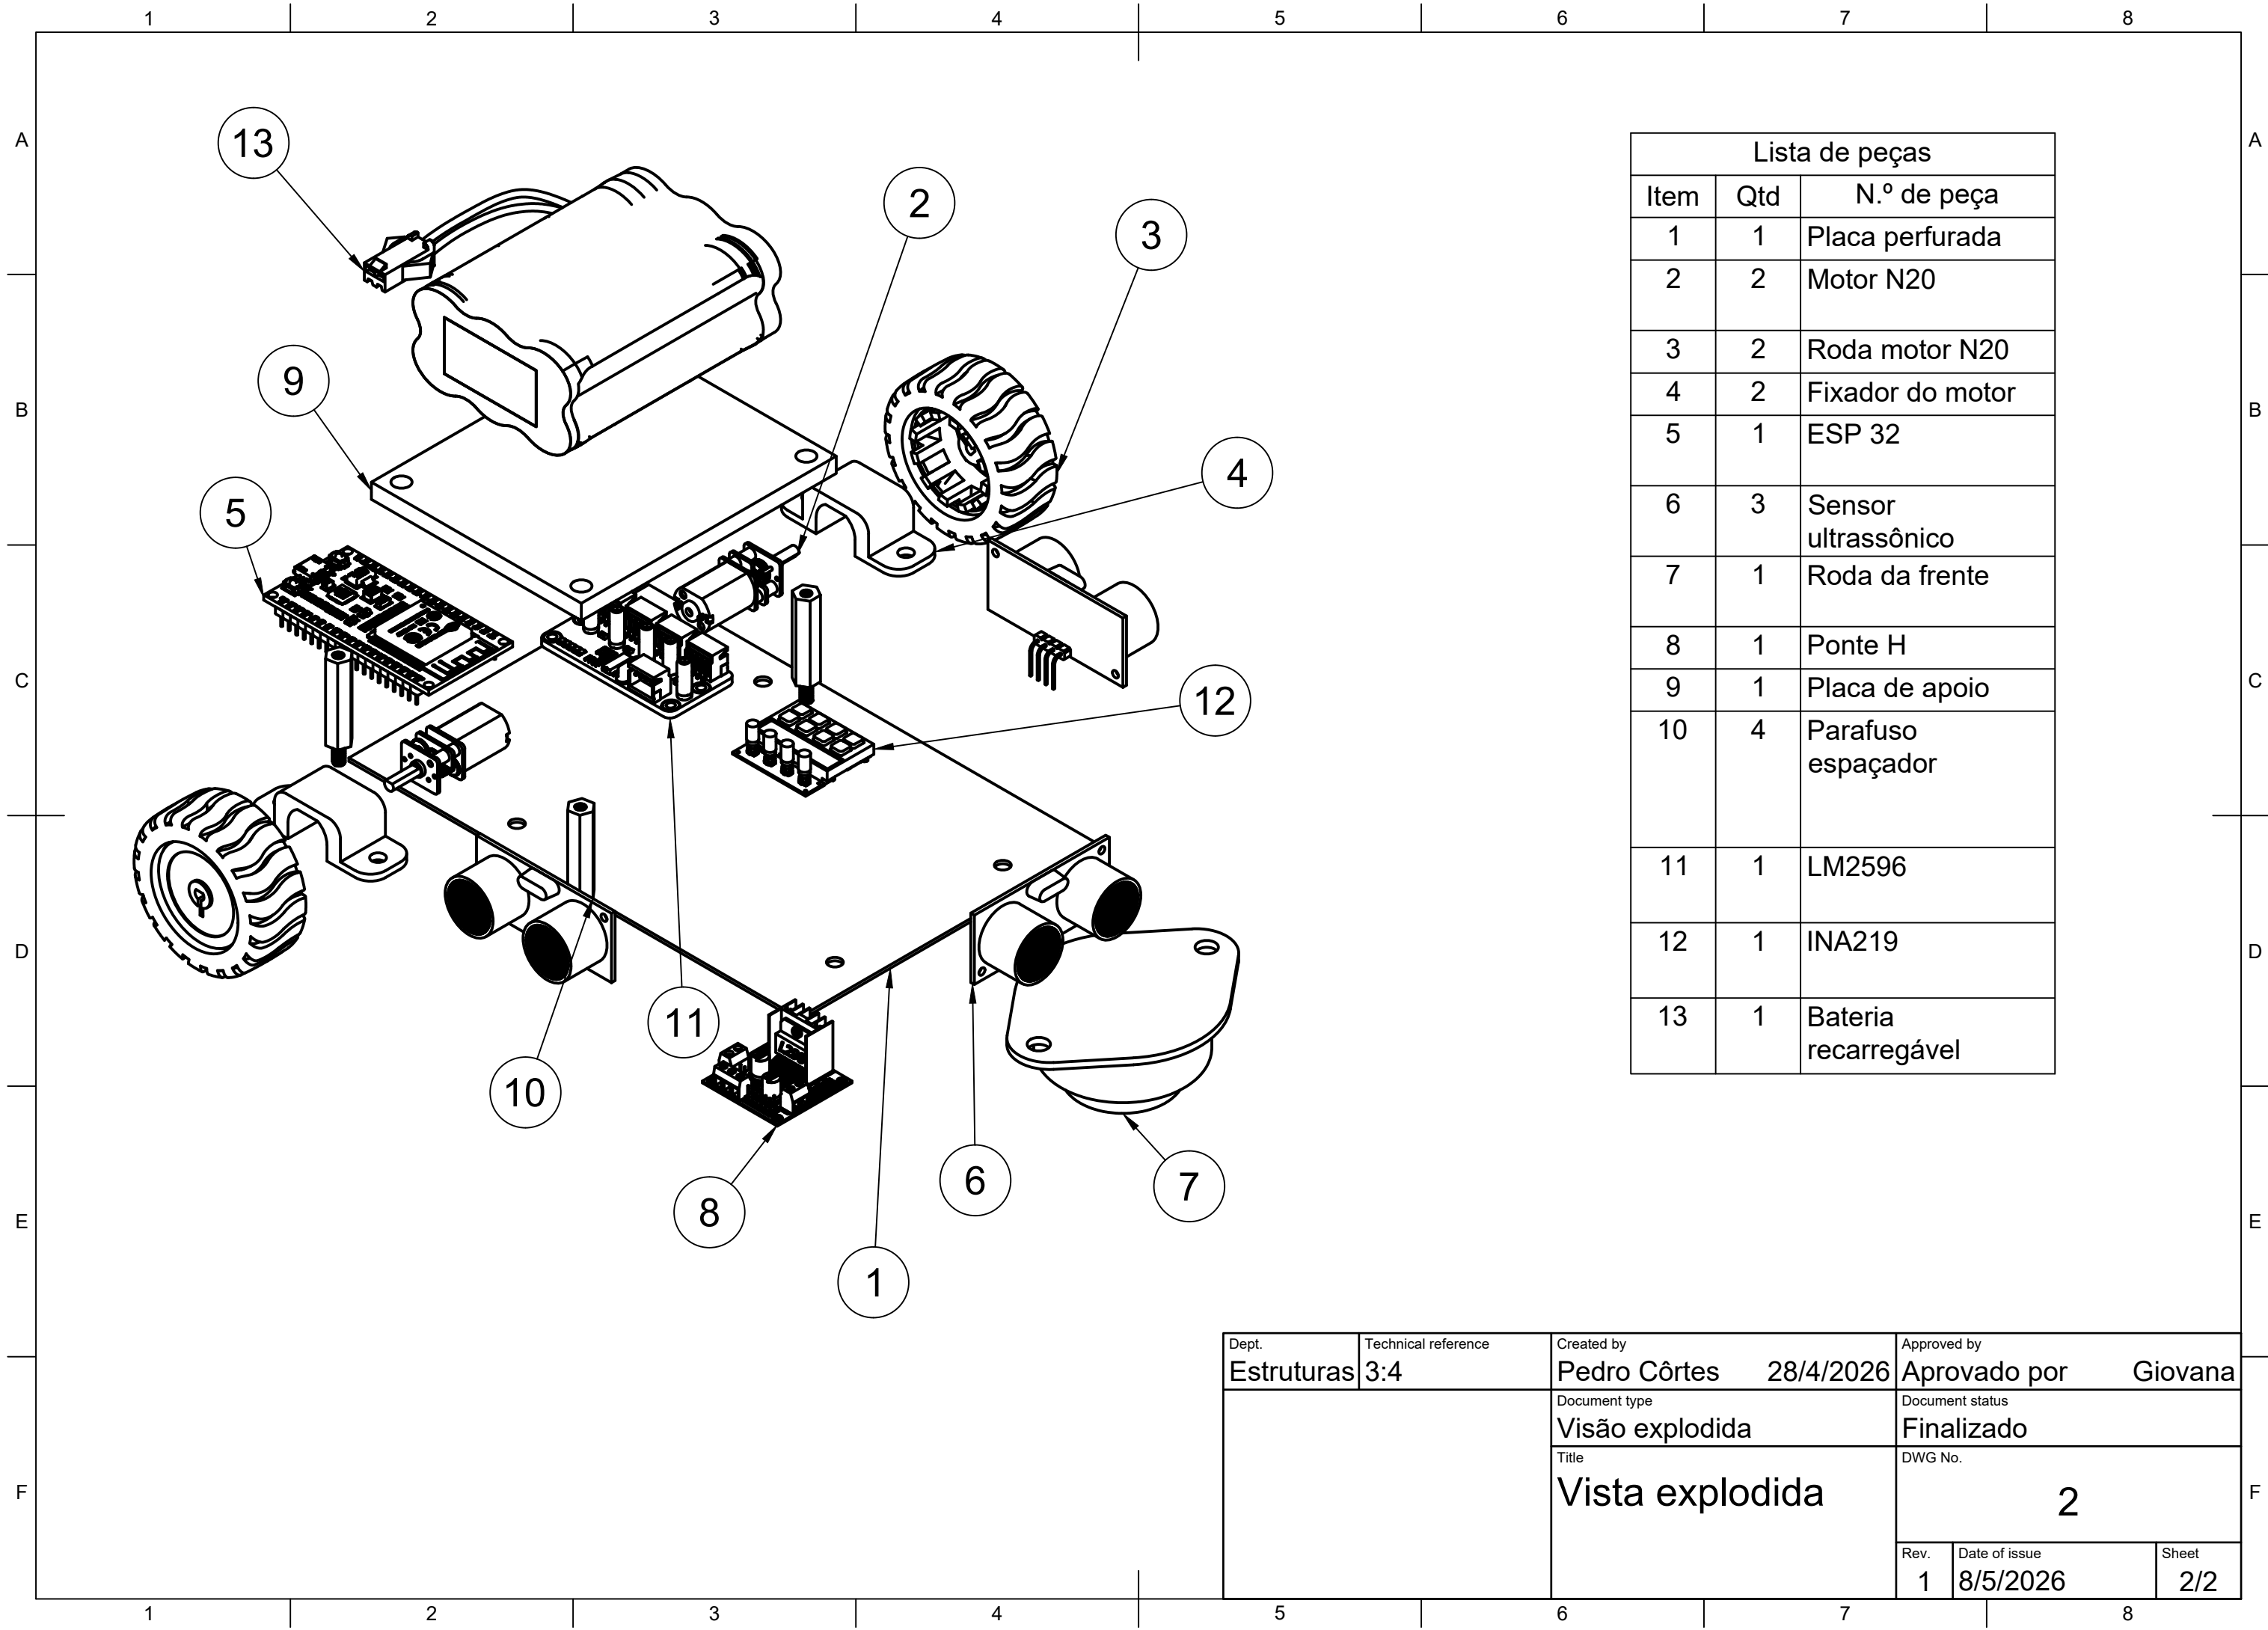

Dept. Estruturas	Technical reference 3:4	Created by Pedro Côrtes 28/4/2026	Approved by Aprovado por Giovana	
		Document type Visão explodida	Document status Finalizado	
		Title Vista explodida	DWG No. 2	
		Rev. 1	Date of issue 8/5/2026	Sheet 2/2